


NAVOTAS POLYTECHNIC COLLEGE ▯ SECOND FLOOR FLOOR PLAN

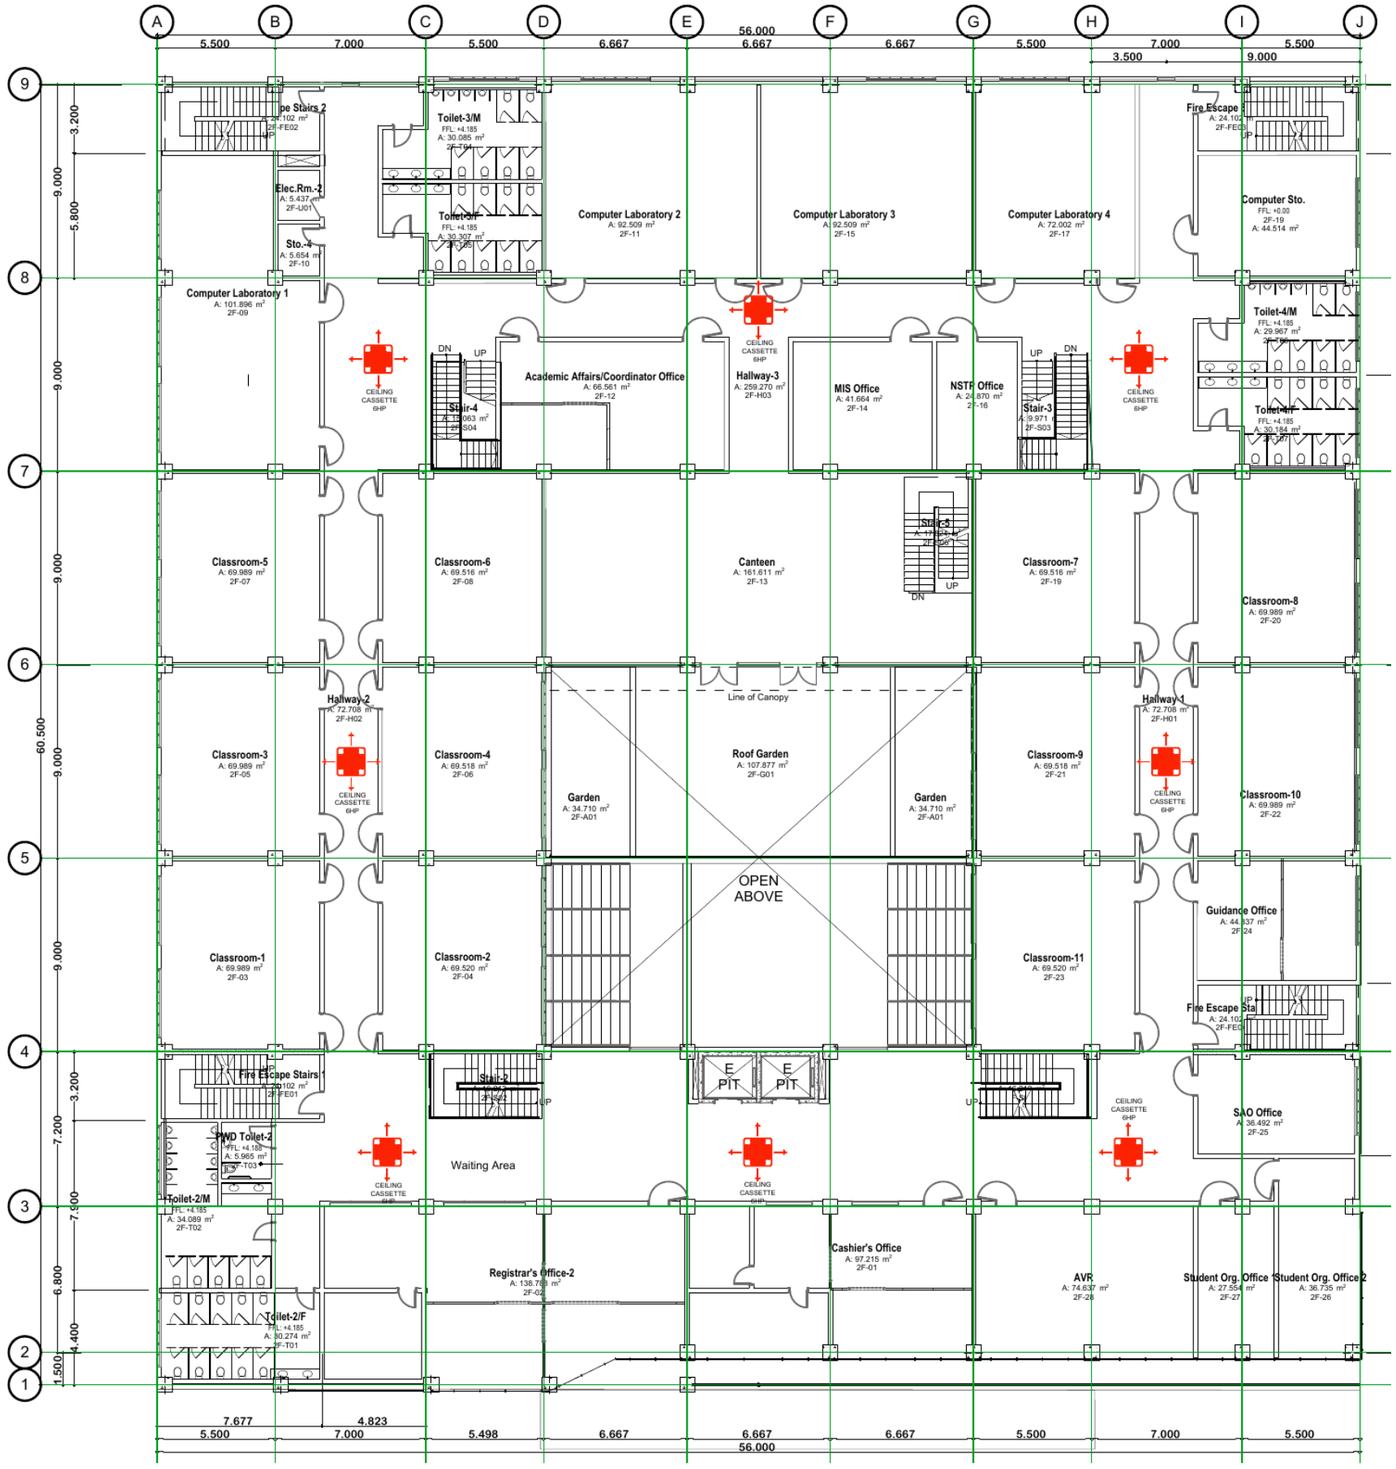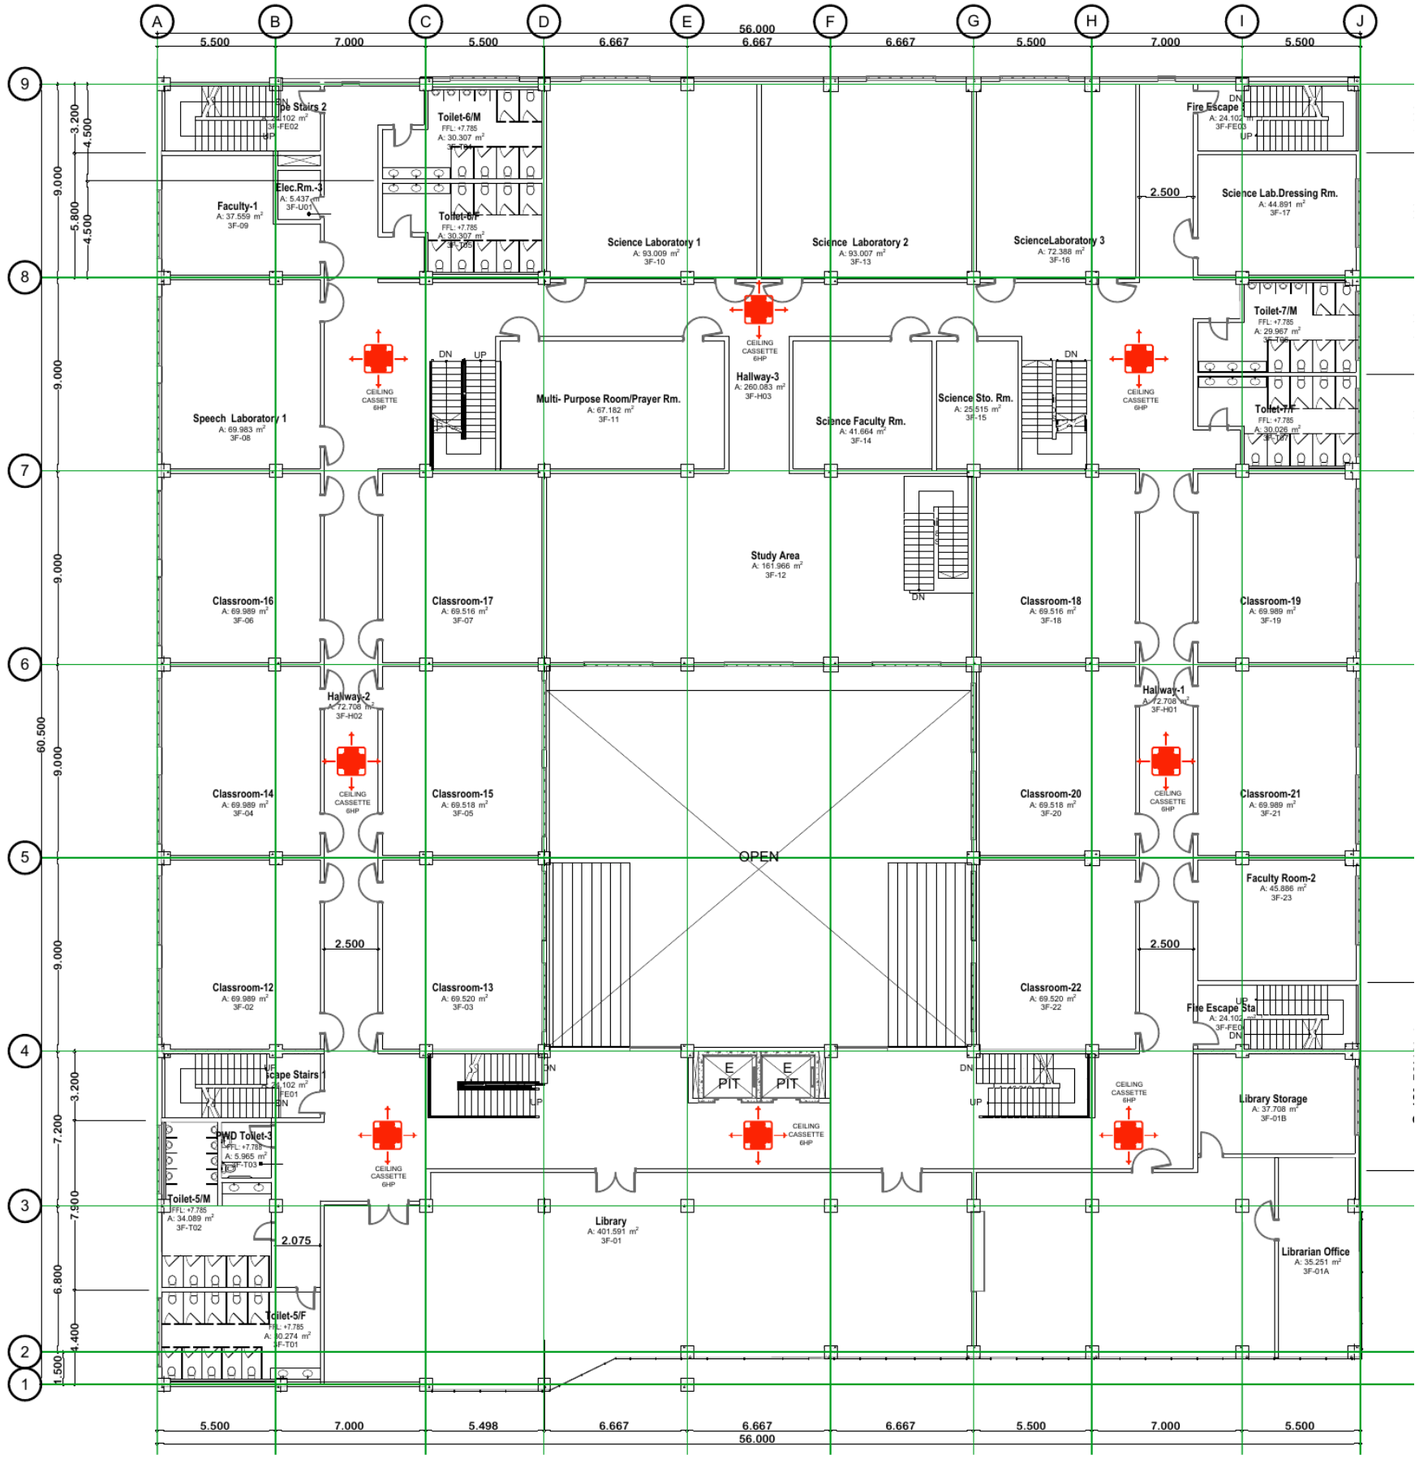

NAVOTAS POLYTECHNIC COLLEGE ⊟ THIRD FLOOR FLOOR PLAN

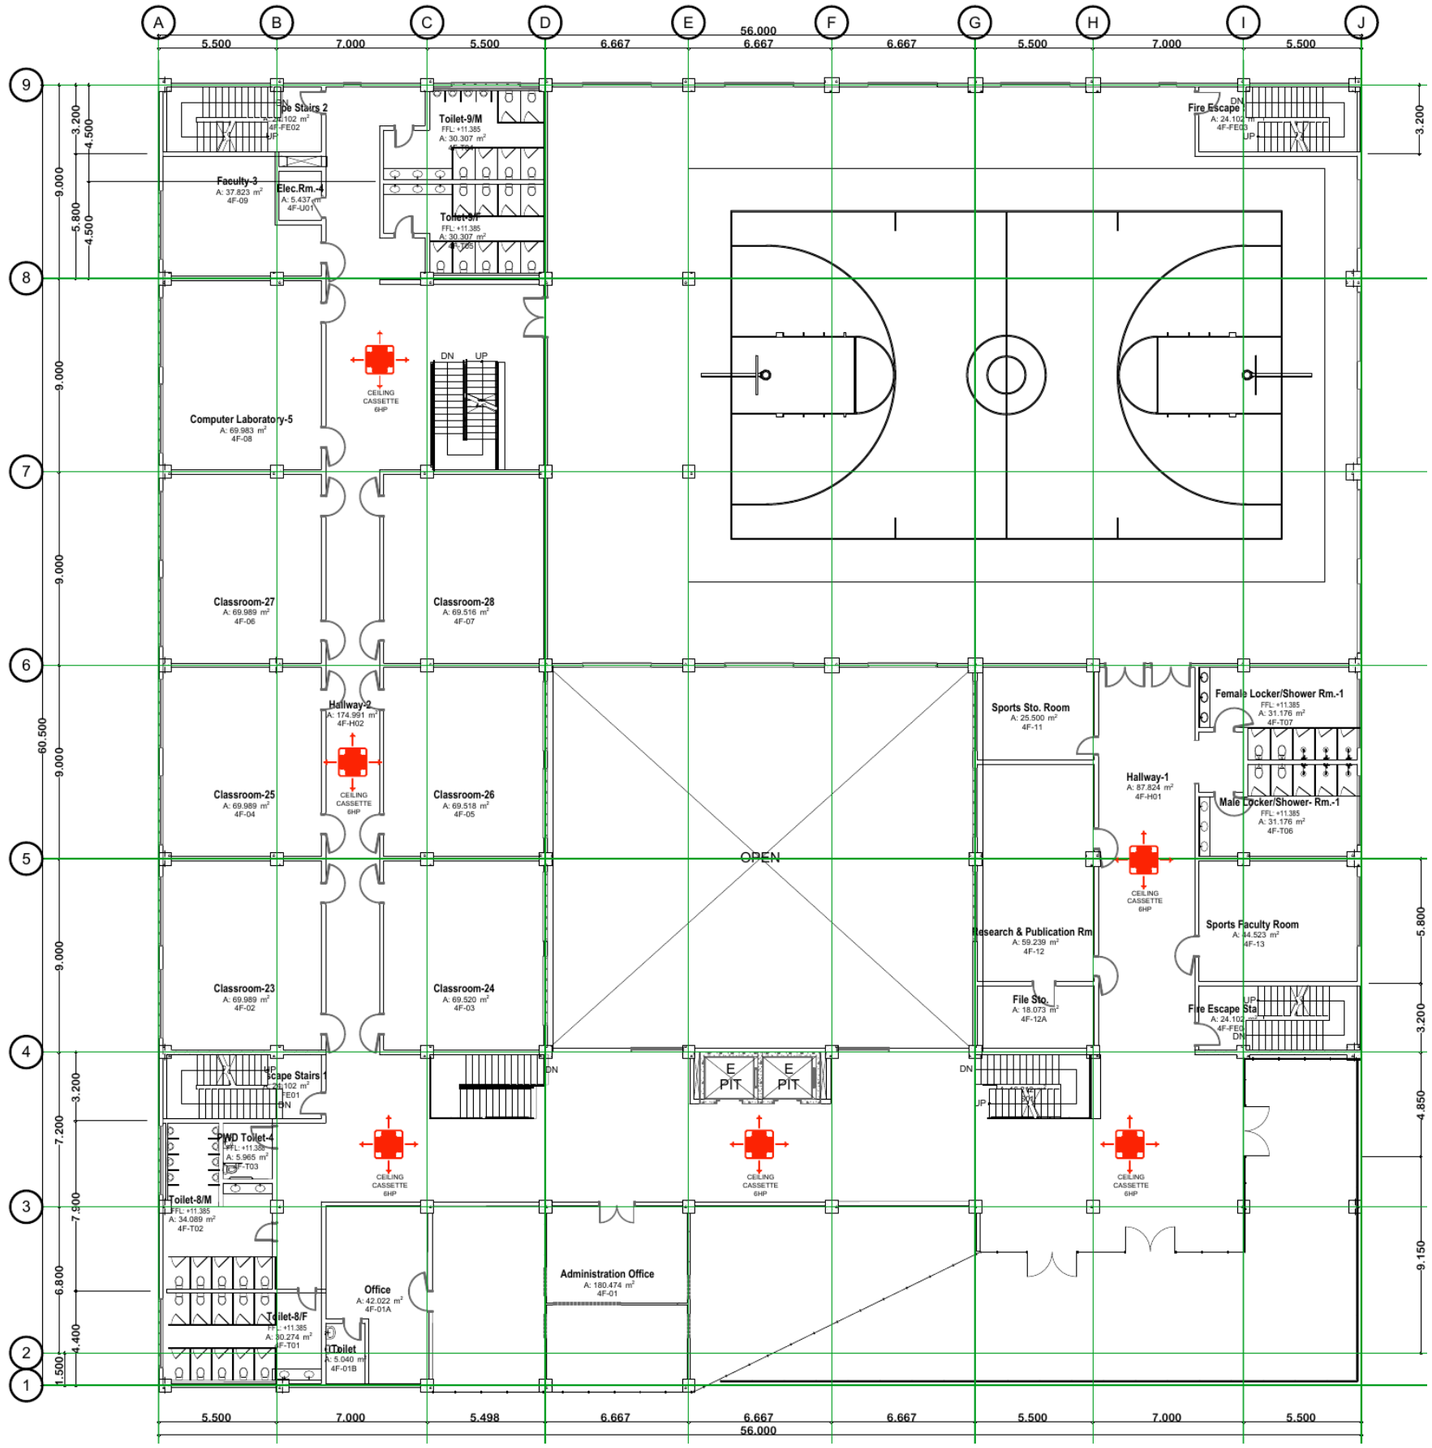


A
B
C
D
E
F
G
H
I
J
56.000
5.500
7.000
5.500
6.667
6.667
6.667
6.667
5.500
7.000
5.500
9
8
7
6
5
4
3
2
1
60.500
9.000
9.000
9.000
9.000
5.800
7.200
7.900
6.800
4.400
1.500
3.200
4.500
4.500
3.200
3.200
5.800
3.200
4.850
9.150
Faculty-3
A: 37.823 m²
4F-09
Elec.Rm.-1
A: 5.437 m²
4F-U01
Toilet-9/M
FFL: +11.385
A: 30.307 m²
4F-T05
Toilet-9/F
FFL: +11.385
A: 30.307 m²
4F-T04
Computer Laboratory-5
A: 69.983 m²
4F-08
CEILING CASSETTE 6HP
DN
UP
Classroom-27
A: 69.989 m²
4F-06
Classroom-28
A: 69.516 m²
4F-07
Hallway-2
A: 174.991 m²
4F-H02
Classroom-25
A: 69.989 m²
4F-04
Classroom-26
A: 69.518 m²
4F-05
OPEN
Classroom-23
A: 69.989 m²
4F-02
Classroom-24
A: 69.520 m²
4F-03
Sports Sto. Room
A: 25.500 m²
4F-11
Research & Publication Rm
A: 59.239 m²
4F-12
File Sto.
A: 18.073 m²
4F-12A
Hallway-1
A: 87.824 m²
4F-H01
Female Locker/Shower Rm.-1
FFL: +11.385
A: 31.176 m²
4F-T07
Male Locker/Shower- Rm.-1
FFL: +11.385
A: 31.176 m²
4F-T06
Sports Faculty Room
A: 94.523 m²
4F-13
Fire Escape
A: 24.102 m²
4F-FE03
Fire Escape Sta
A: 24.102
4F-FE0
Fire Escape Stairs 2
A: 26.102 m²
4F-FE02
Fire Escape Stairs 1
A: 26.102 m²
4F-FE01
PWD Toilet-4
FFL: +11.385
A: 5.965 m²
4F-T03
Toilet-8/M
FFL: +11.385
A: 34.089 m²
4F-T02
Toilet-8/F
FFL: +11.385
A: 30.274 m²
4F-T01
Office
A: 42.022 m²
4F-01A
Toilet
A: 5.040 m²
4F-01B
Administration Office
A: 180.474 m²
4F-01
E PIT
E PIT
5.500
7.000
5.498
6.667
6.667
6.667
56.000

NAVOTAS POLYTECHNIC COLLEGE ROOF DECK FLOOR PLAN

